


DETALLES CONSTRUCTIVOS

panel MG®


Sistemas Constructivos MG
S.A. de C.V.

CIMENTACIÓN

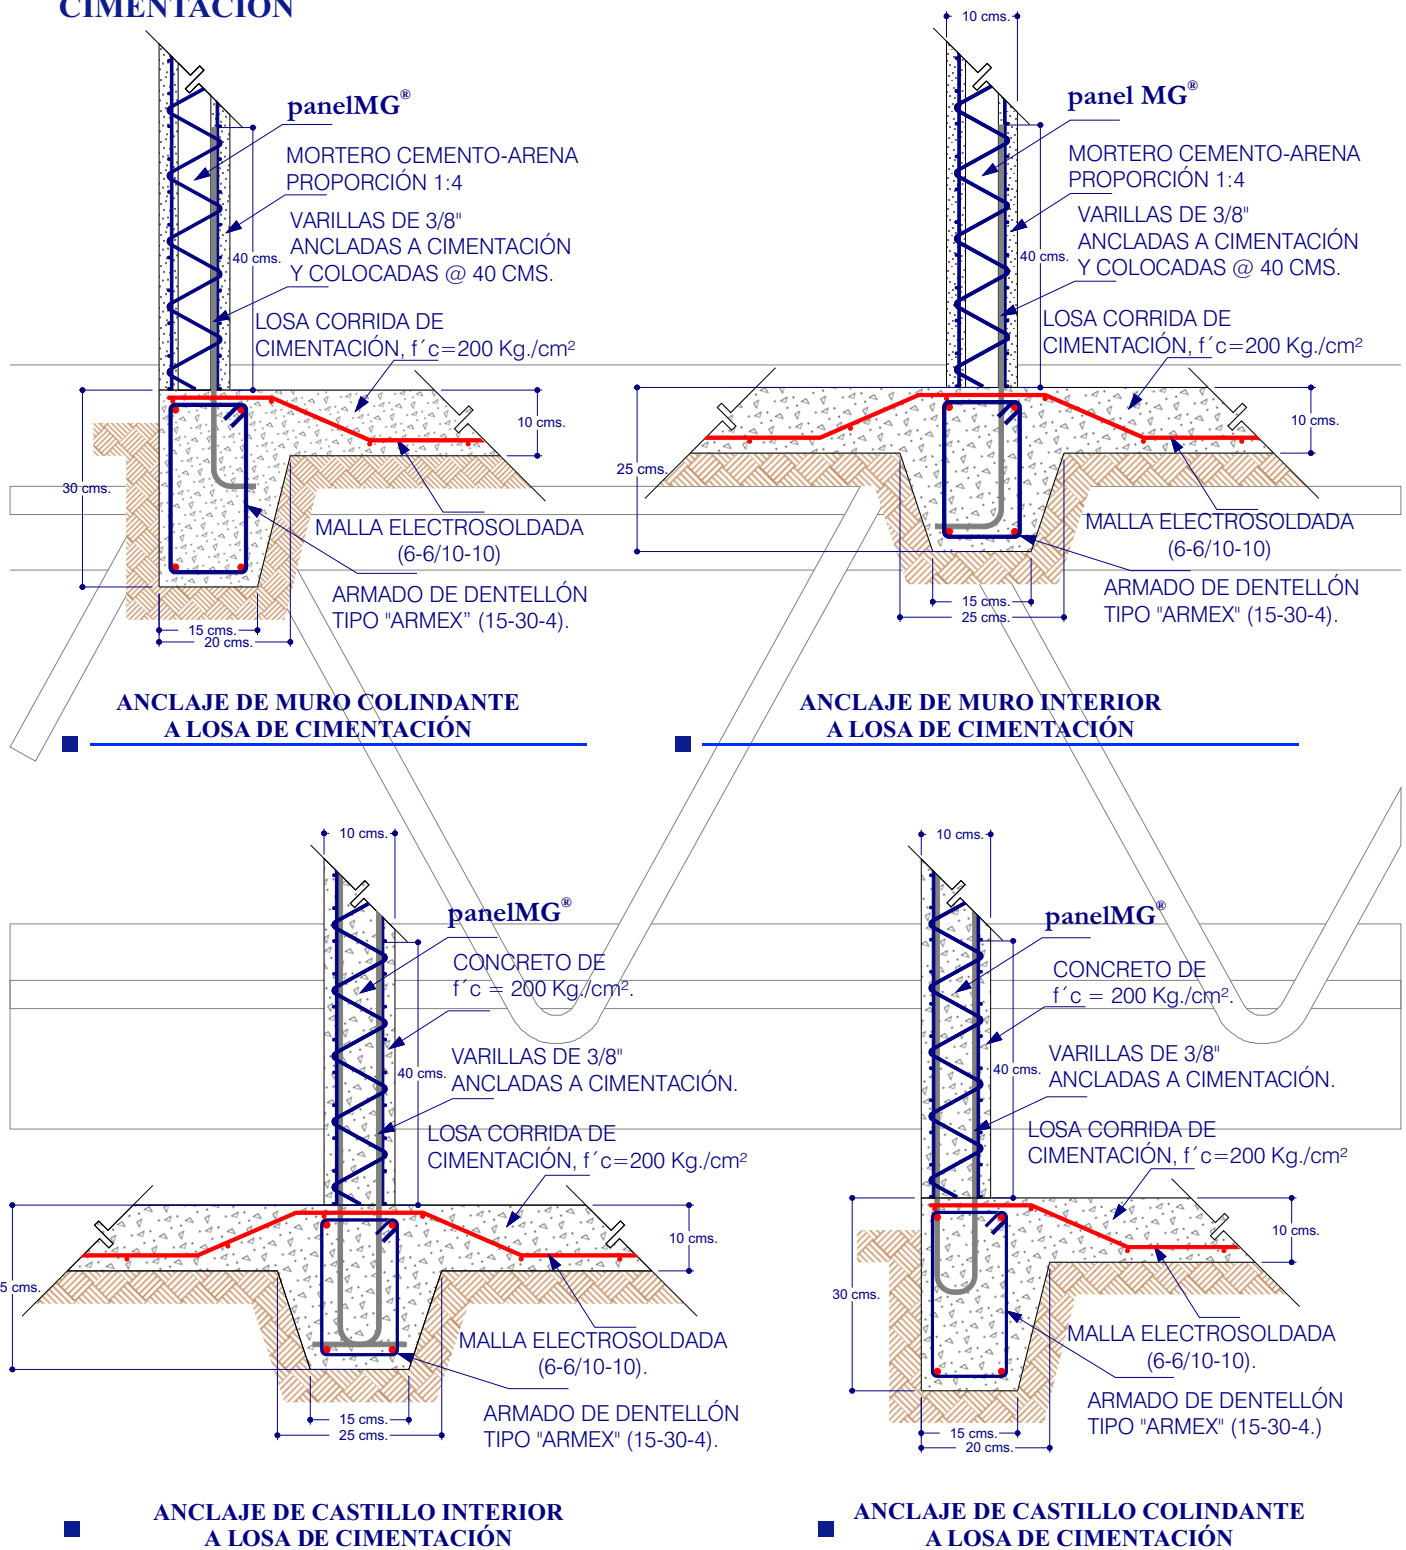


DETALLES CONSTRUCTIVOS

CIMENTACIÓN

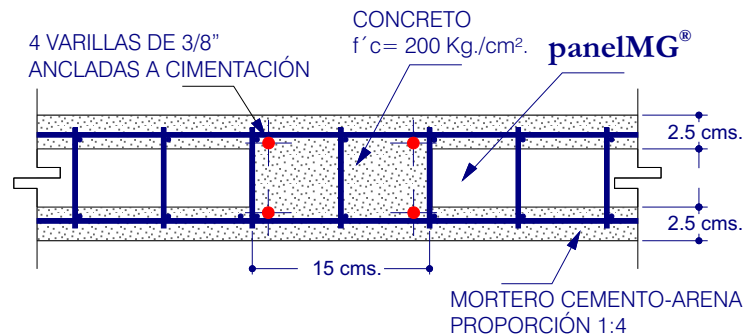


CASTILLO INTEGRADO AL PANEL

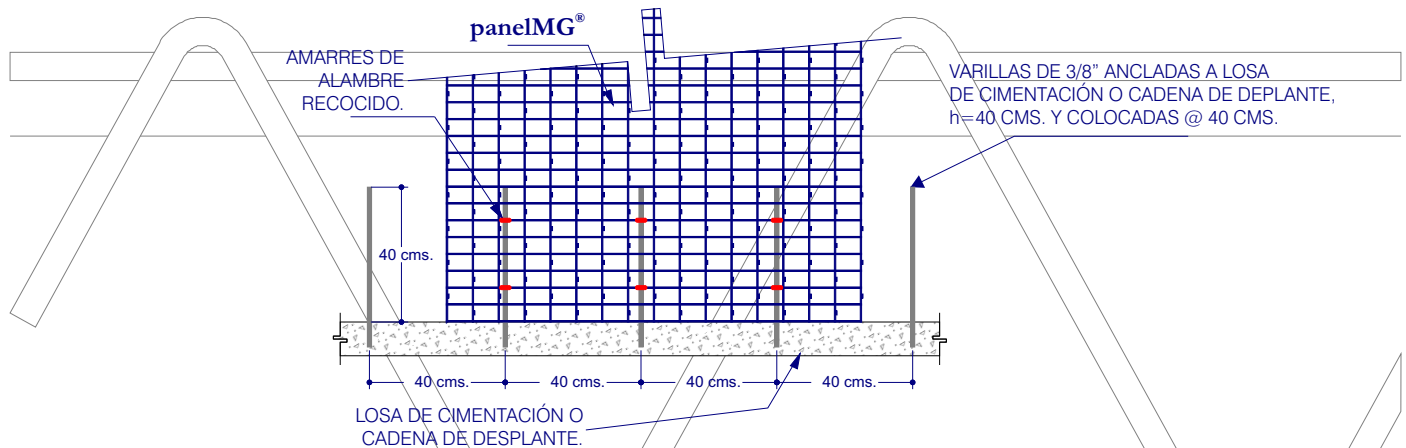

ANCLAJE DE MUROS DE PANEL

MUROS

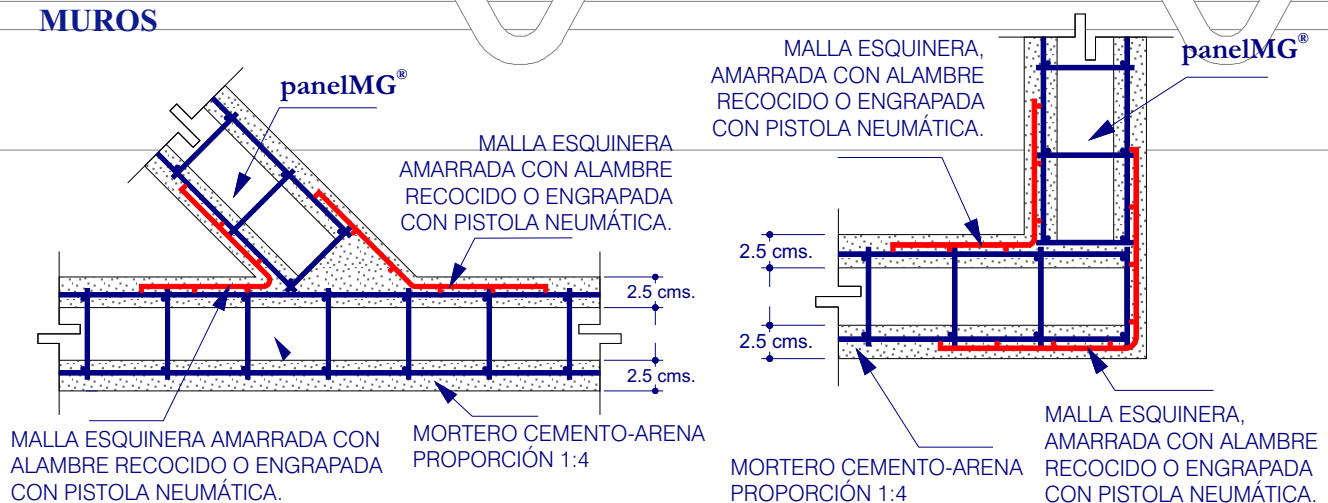


UNIÓN DE MUROS DIAGONALES

UNIÓN DE MUROS EN ESQUINA

DETALLES CONSTRUCTIVOS


MUROS

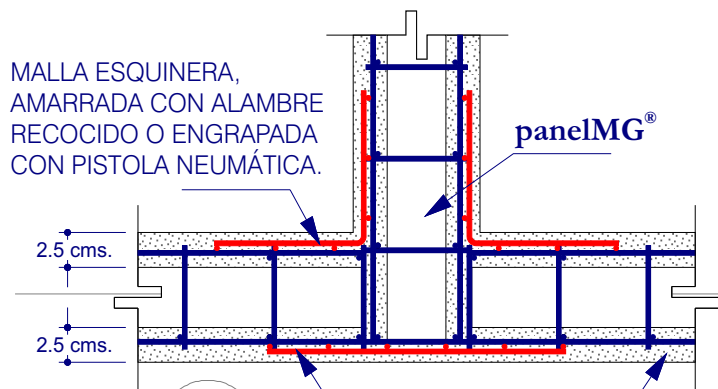

MALLA UNIÓN AMARRADA CON ALAMBRE RECOCIDO O ENGRAPADA CON PISTOLA NEUMÁTICA.


MORTERO CEMENTO-ARENA PROPORCIÓN 1:4

UNIÓN DE MUROS PERPENDICULARES

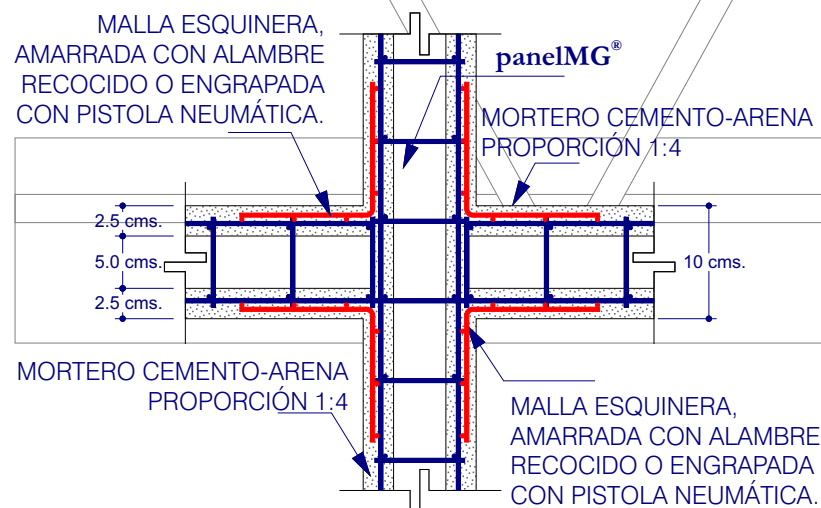


UNIÓN CRUCE DE MUROS PERPENDICULARES

AMARRE DE ALAMBRE RECOCIDO O GRAPAS, @ 15 CMS. EN FORMA ALTERNADA PARA UNIR MALLAS CON PANEL.

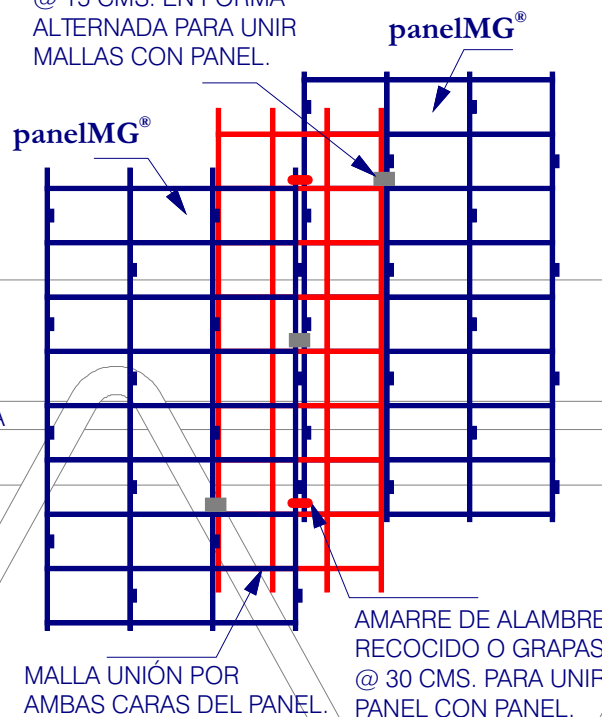


AMARRES DE MALLAS Y PANELES

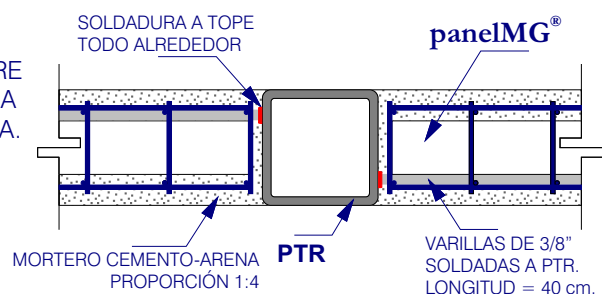

ANCLAJE DE PANEL A POSTE DE PTR.

DETALLES CONSTRUCTIVOS

MUROS

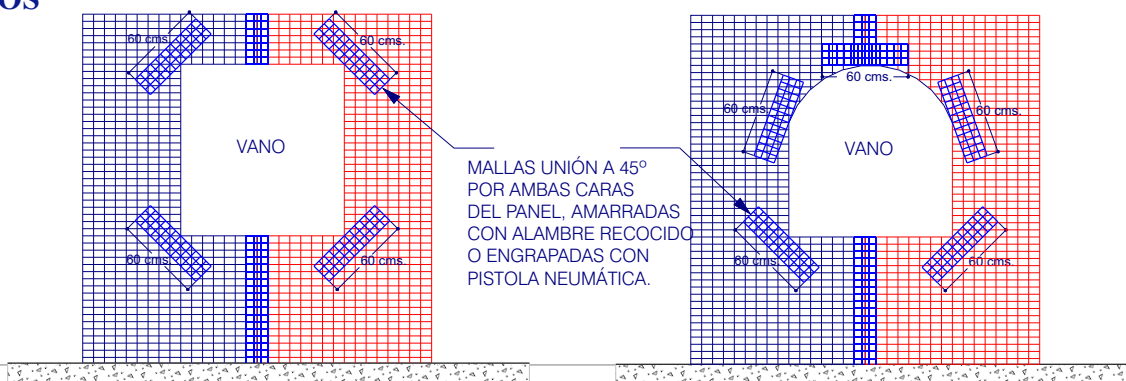

REFUERZO DE MARCOS DE VENTANAS

LOSAS

MALLA UNIÓN POR AMBAS CARAS, PARA UNIR PANEL CON PANEL, AMARRADA CON ALAMBRE RECOCIDO O ENGRAPADA CON PISTOLA NEUMÁTICA.

CAPA DE COMPRESIÓN CONCRETO DE 200 Kg./cm².

panelMG®

5.0 cms.

2.5 cms.

MORTERO CEMENTO-ARENA PROPORCIÓN 1:4

panelMG

UNIÓN DE PANEL EN LOSAS

ANCLA DE 3/8" SOLDADAS A VIGA Y COLOCADAS @ 60 cm

CAPA DE COMPRESIÓN CONCRETO DE 200 kg/cm²

VARILLAS DE 3/8" EN CAPA DE COMPRESIÓN

panelMG®

MORTERO CEMENTO-ARENA PROPORCIÓN 1:4

VIGA DE ACERO.

ARMADO DE LOSA VARILLAS DE 3/8"

APOYO DE LOSA INCLINADA EN VIGA DE ACERO

ESCUADRAS DE VARILLAS DE 3/8".

MALLA ESQUINERA PARA UNIR PANEL CON PANEL.

CAPA DE COMPRESIÓN CONCRETO DE 200 kg./cm²

VARILLAS DE 3/8" EN CAPA DE COMPRESIÓN

5.0 cms.

2.5 cms.

MALLA ESQUINERA, AMARRADA CON ALAMBRE RECOCIDO O ENGRAPADA CON PISTOLA NEUMÁTICA.

ARMADO DE LOSA VARILLAS DE 3/8"


panelMG®

MORTERO CEMENTO-ARENA PROPORCIÓN 1:4

UNIÓN DE MURO CON VOLADIZO Y PRETIL

DETALLES CONSTRUCTIVOS

LOSAS

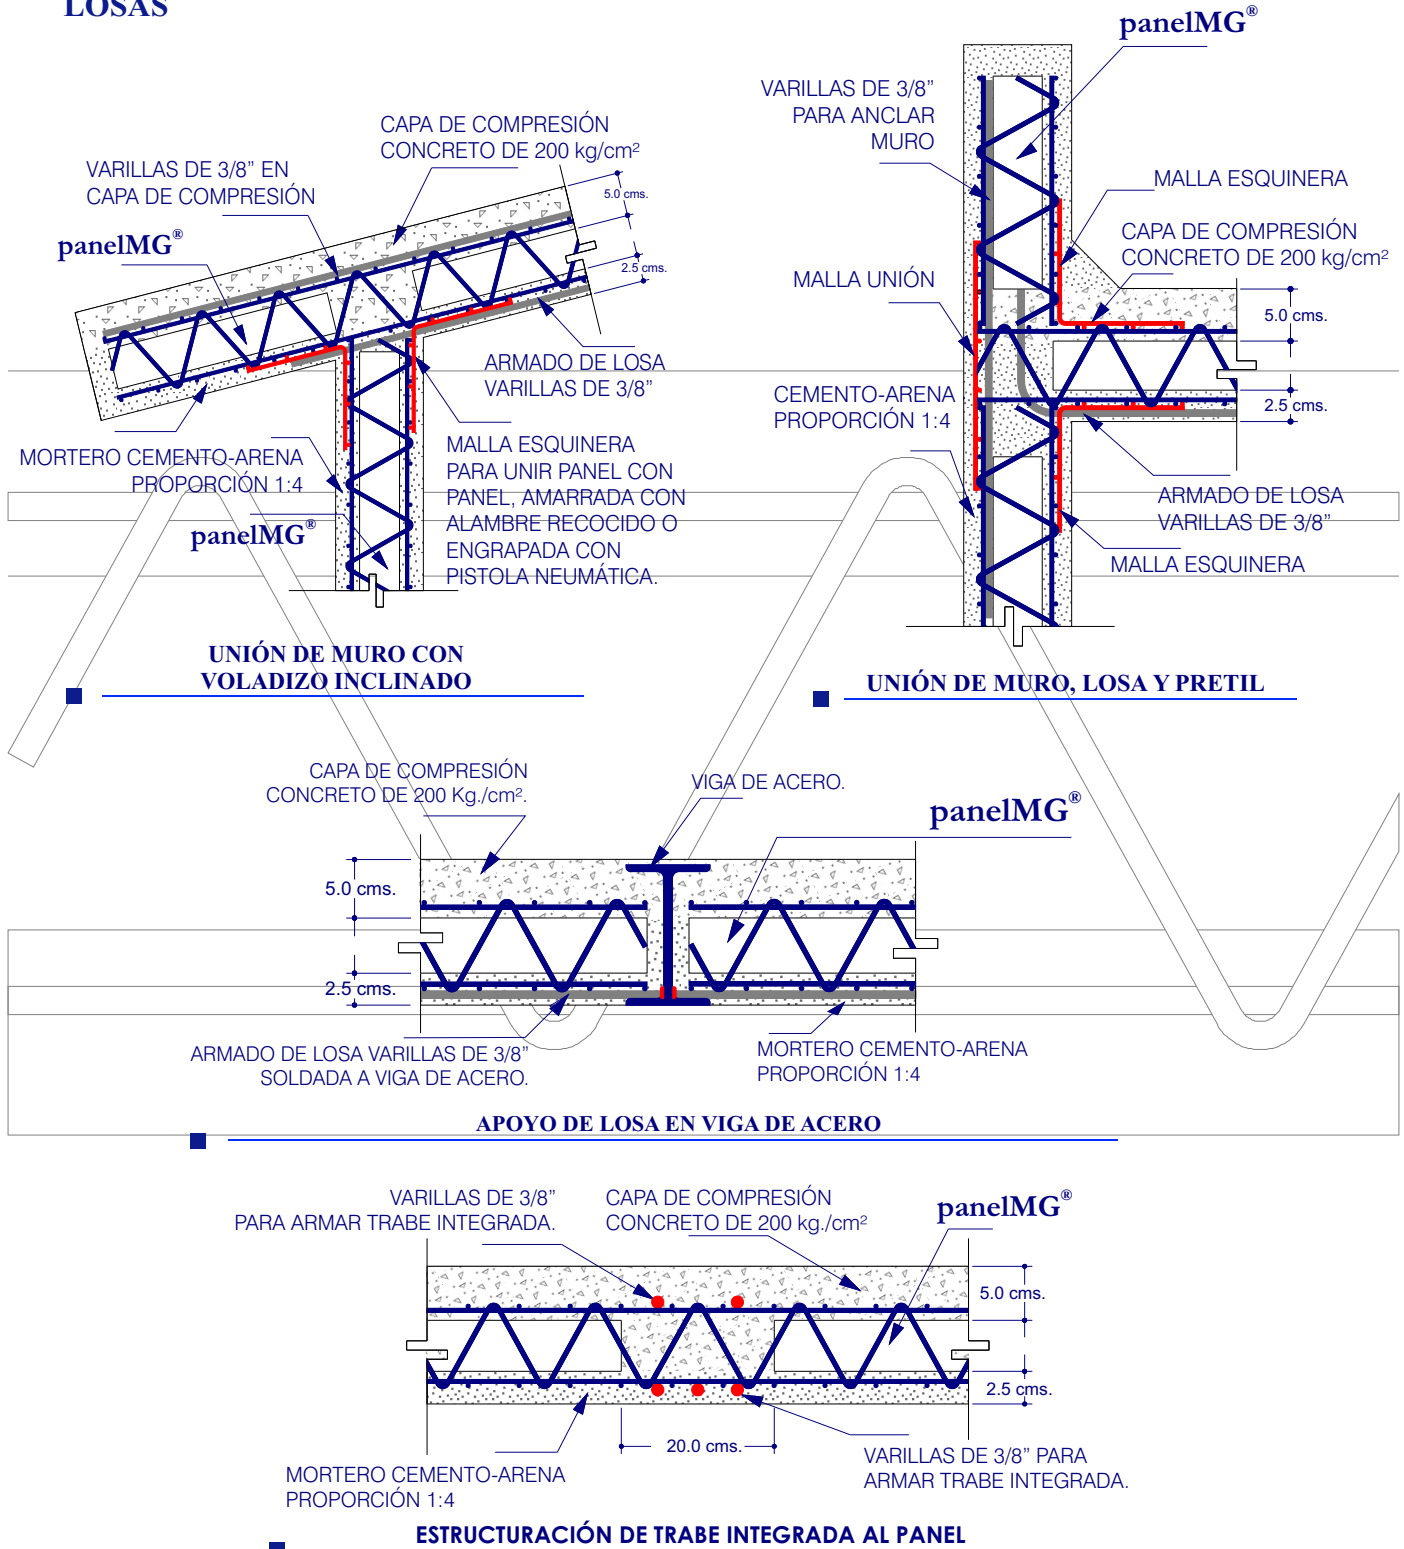

DETALLES CONSTRUCTIVOS

LOSAS


MACILLA ESQUINERA PARA UNIR PANEL CON PANEL, AMARRADA CON ALAMBRE RECOCIDO O ENGRAPADA CON PISTOLA NEUMÁTICA.

CAPA DE COMPRESIÓN CONCRETO DE 200 kg/cm²

VARILLAS DE 1/2" REFUERZO LONGITUDINAL.

ANCLAJE DEL ARMADO DE LOSA


MORTERO CEMENTO-ARENA PROPORCIÓN 1:4

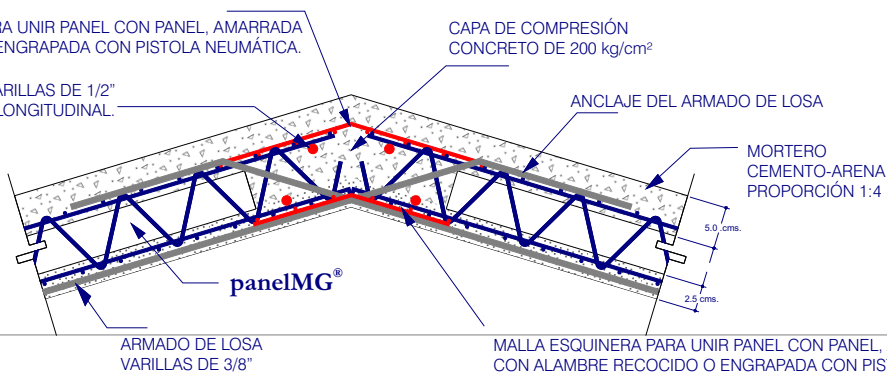

ARMADO DE LOSA VARILLAS DE 3/8"

MACILLA ESQUINERA PARA UNIR PANEL CON PANEL, AMARRADA CON ALAMBRE RECOCIDO O ENGRAPADA CON PISTOLA NEUMÁTICA.

UNIÓN DE CUMBRERAS

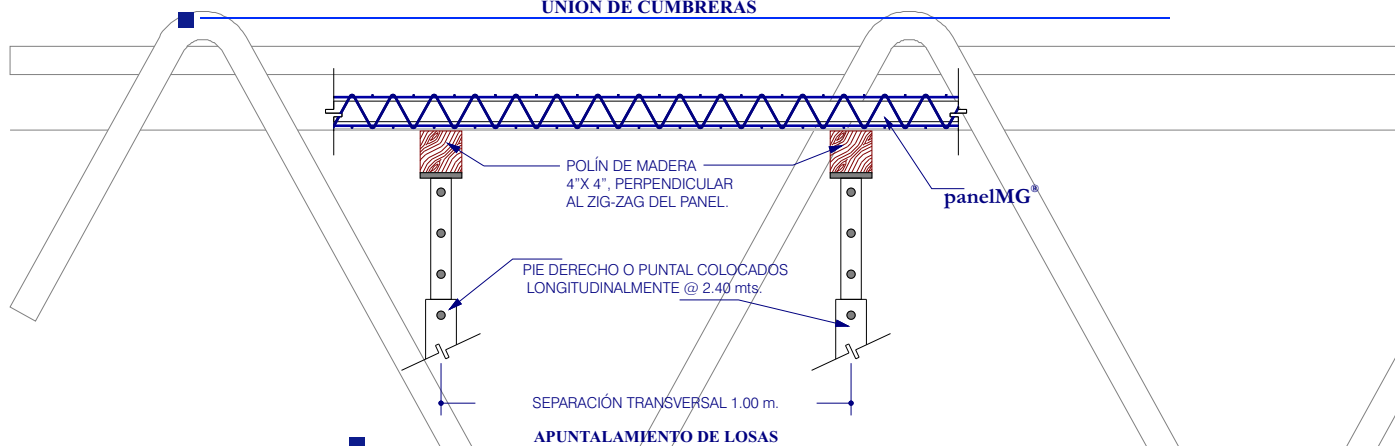

APUNTALAMIENTO DE LOSAS


MUROS DIVISORIOS

RECIBIDOR DE CORTANTE COLOCADO @ 60 cm


panelMG®

VARILLAS ANCLADAS A LOSA DE CONCRETO COLOCADAS @ 40 cm ALTURA 40 cm

LOSA DE CONCRETO

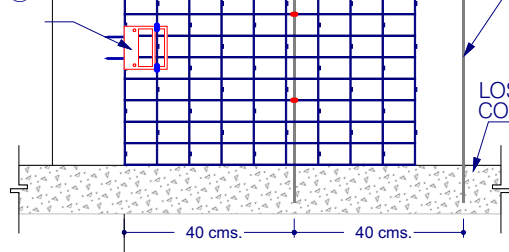


ANCLAJE DE MURO A LOSA DE CONCRETO CON ANCLAS DE VARILLAS

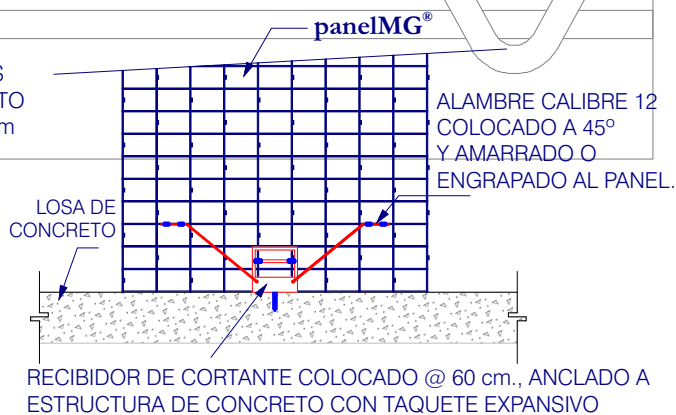


ANCLAJE DE MURO A LOSA DE CONCRETO CON RECIBIDOR DE CORTANTE

DETALLES CONSTRUCTIVOS

MUROS DIVISORIOS

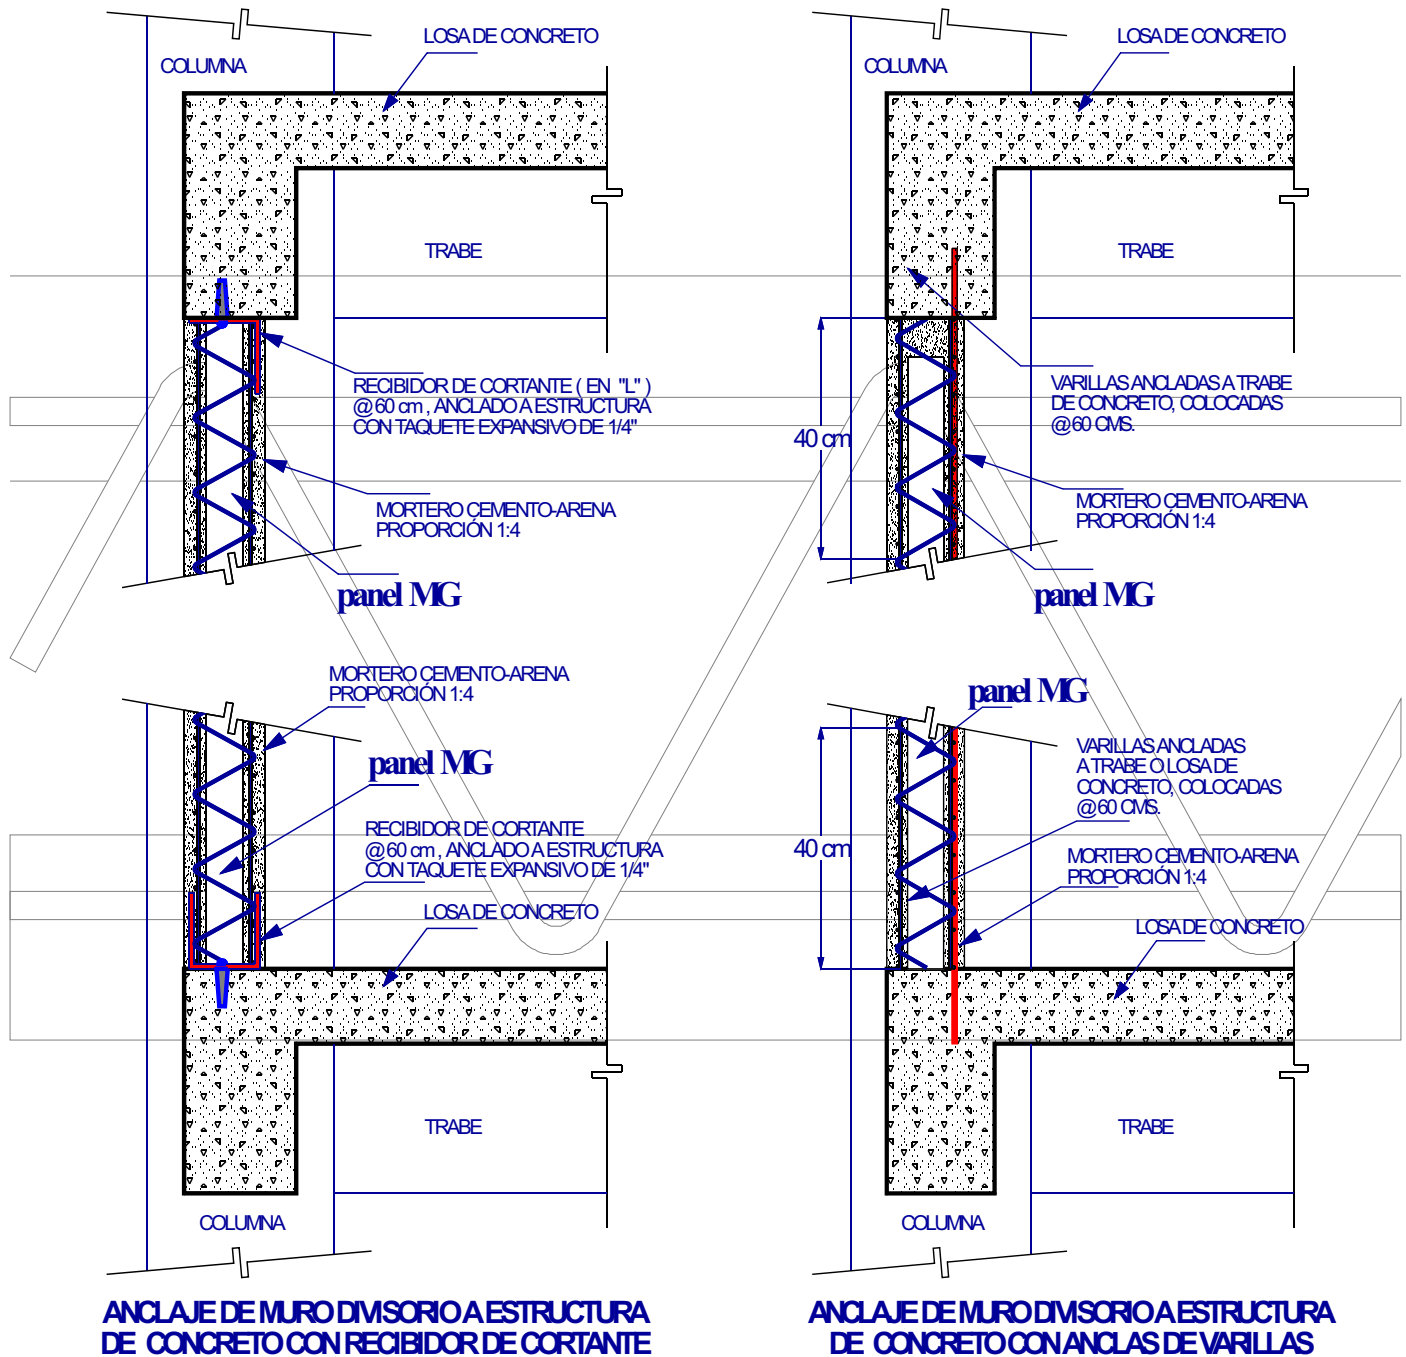

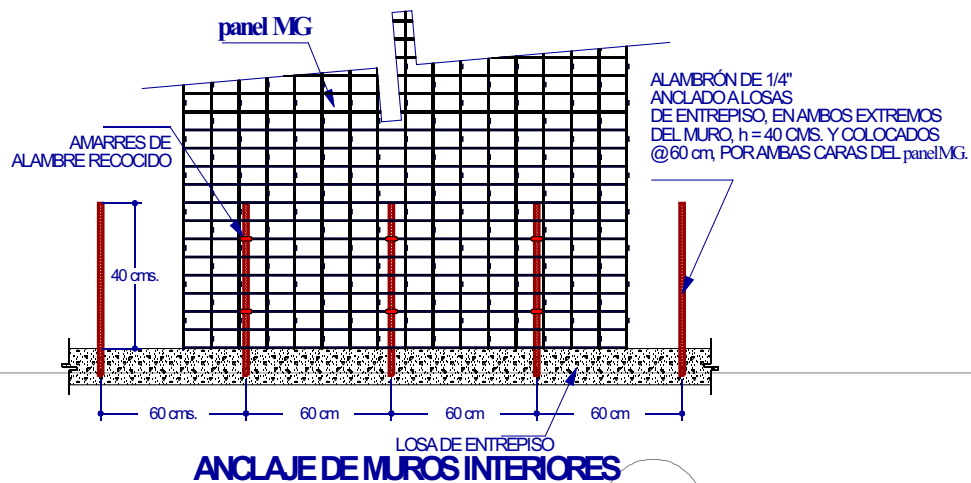

MALLA ESQUINERO PARA UNIR PANEL CON
 PANEL, AMARRADA CON ALAMBRE RECOCIDO O
 ENGRAPADA CON PISTOLA NEUMÁTICA.

VARILLAS SOLDADAS A PTR, PARA AMARRAR EL PANEL

ARMAZÓN DE PTR SOPORTE DEL PANEL

PLACA DE ACERO LOSA DE CONCRETO

TRABE DE ACERO

ARMAZÓN DE PTR SOLDADO A ESTRUCTURA DE ACERO

MALLA ESQUINERO PARA UNIR PANEL CON
 PANEL, AMARRADA CON ALAMBRE RECOCIDO
 O ENGRAPADA CON PISTOLA NEUMÁTICA.

MALLA ESQUINERO PARA UNIR PANEL CON
PANEL, AMARRADA CON ALAMBRE RECOCIDO
O ENGRAPADA CON PISTOLA NEUMÁTICA.

COLUMNA DE ACERO

APOYO DE FALDÓN-PRETL A ESTRUCTURA DE ACERO